

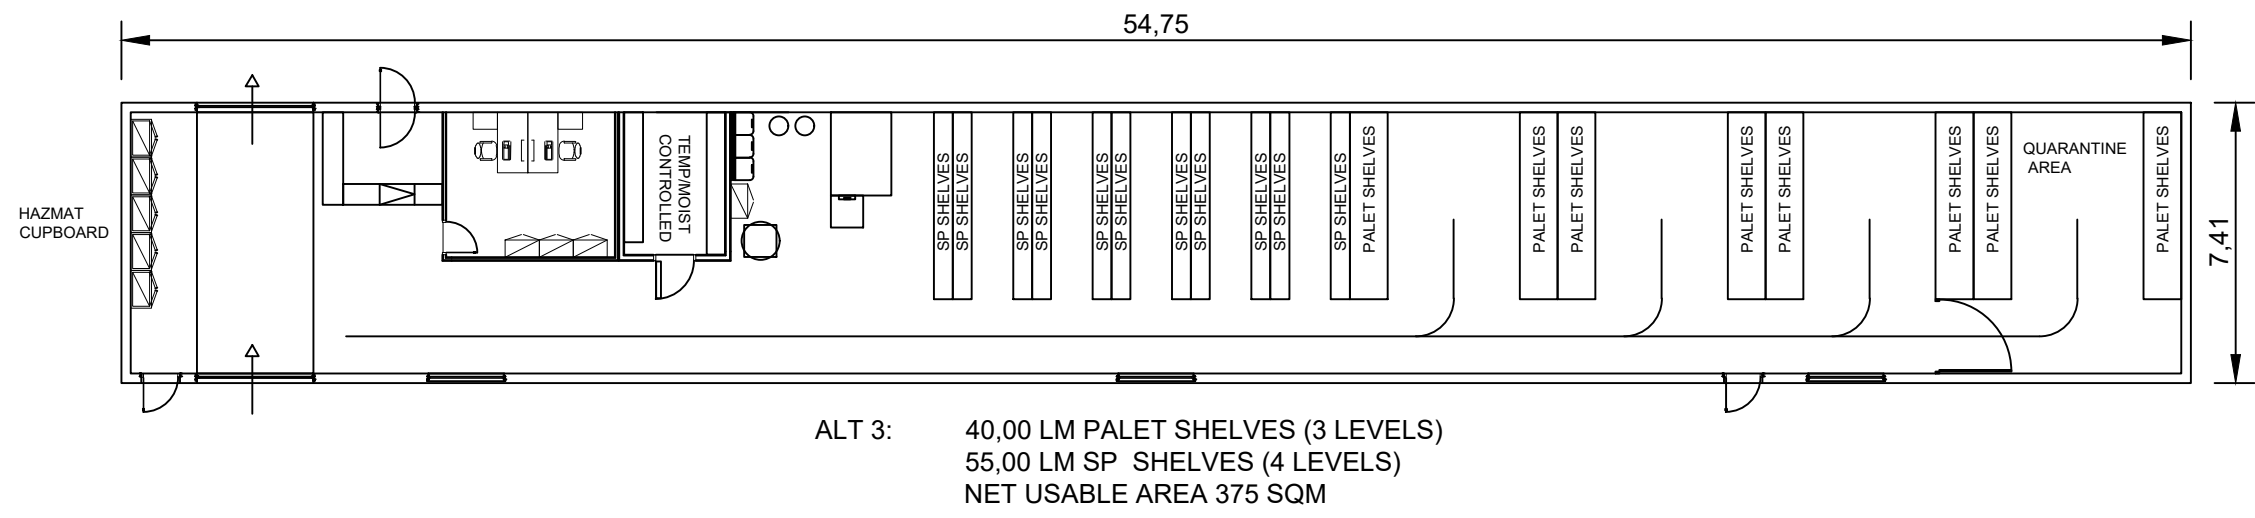


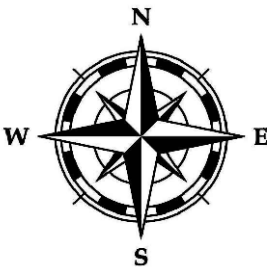

STORAGE BASIC DESIGN OPTIONS

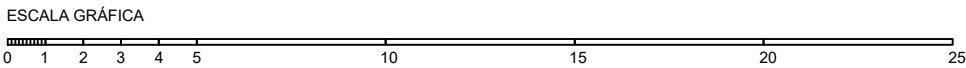

NOTAS
1. Plano de distribución en planta del almacén longitudinal a cota +0,00
2. Estanterías de palets: 3 niveles, 40 lm lineales totales
3. Estanterías SP: 4 niveles, 55 lm lineales totales
4. Superficie útil del almacén: 347 m²
5. Los sensores de presencia para control de iluminación se ubicarán en los pasillos entre estanterías
6. Referencias de zonas según ficheros CAD entregados por la propiedad

 AIRBUS		UNIVERSIDAD DE MÁLAGA				
		PROYECTO DE INGENIERÍA: Iluminación automatizada y sistema de videovigilancia del hangar 3 de producción de aviones. Fábrica AIRBUS - Tablada (Sevilla)				
PROMOTOR: Airbus S.A.S.		LOCALIZACIÓN: Av. Maestranza Aérea, Nº 17, C.P. 41011, Sevilla (España)				
PLANO Nº: 1.2.2.	DISTRIBUCIÓN EN PLANTA DEL ALMACÉN LONGITUDINAL					
AUTOR: José María Tendero Navajas		REVISOR: Maya Ruiz Díaz		ESCALA: 1:200	COTAS EN: m	AUTOR:
TITULACIÓN: GRADO EN INGENIERÍA ELECTRÓNICA, ROBÓTICA Y MECATRÓNICA		FECHA: JUNIO/2026			REVISOR:	
					Fdo.:	