

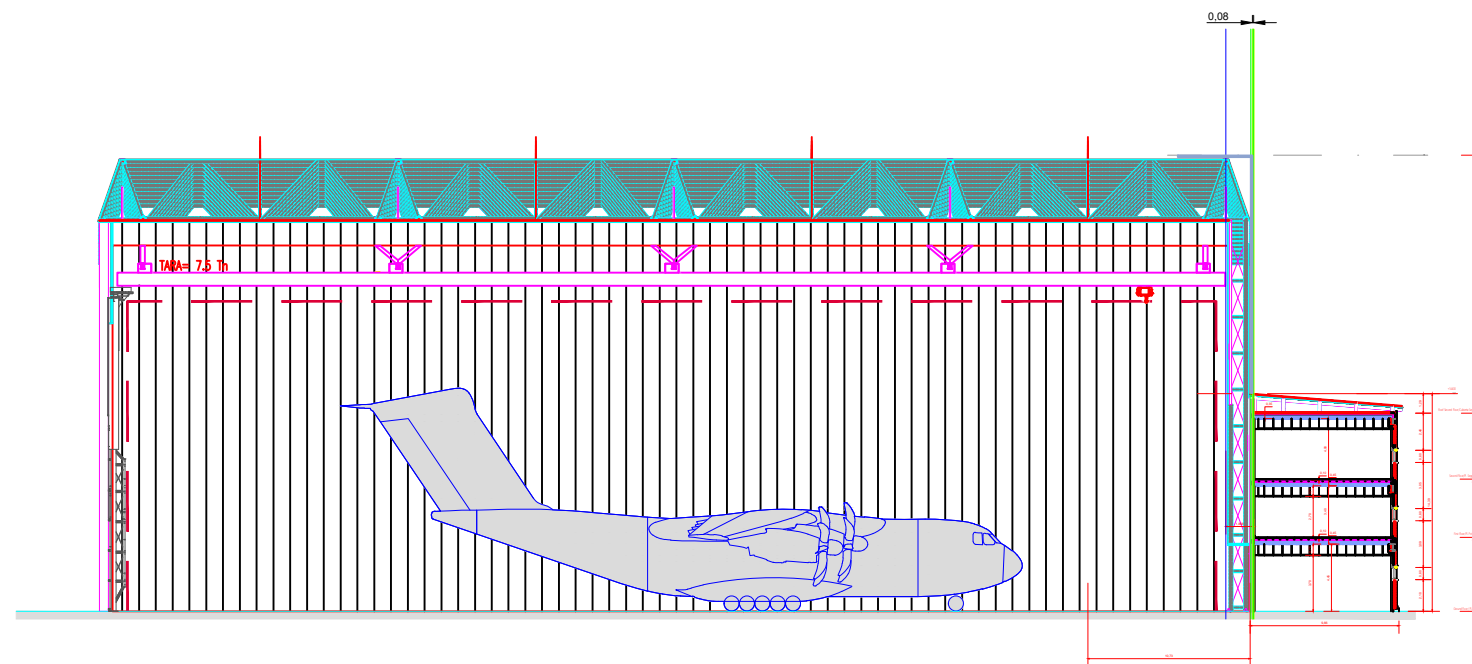


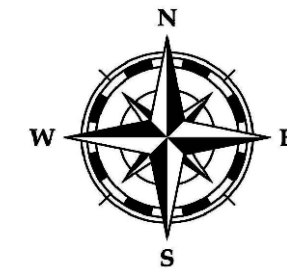

NOTAS

1. Sección transversal del hangar y zona de oficinas
2. Cota $\pm 0,00$ corresponde a nivel de planta baja acabada
3. Altura Planta Baja: 4,90 m
4. Altura Planta Primera: 8,75 m
5. Altura Cubierta zona oficinas: 13,10 m
6. Altura libre almacén longitudinal: 4,00 m
7. Anchura zona de oficinas: 33,60 m
8. Ver plano 1.2.1 para distribución en planta

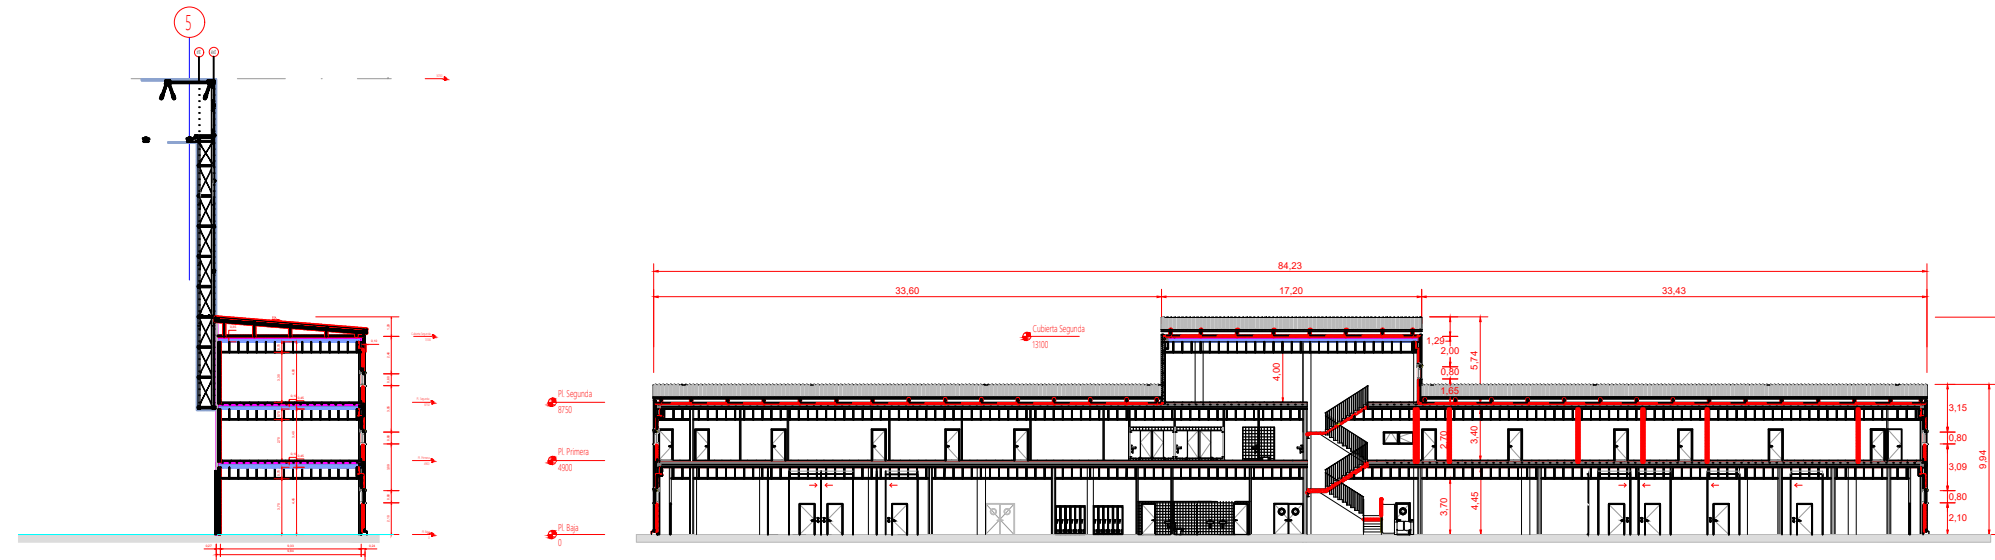

UNIVERSIDAD DE MÁLAGA

PROYECTO DE INGENIERÍA:

Iluminación automatizada y sistema de videovigilancia del hangar 3 de producción de aviones. Fábrica AIRBUS - Tablada (Sevilla)

PROMOTOR:
Airbus S.A.S.

LOCALIZACIÓN:
Av. Maestranza Aérea, Nº 17, C.P. 41011, Sevilla (España)

PLANO Nº:
1.2.3.

SECCIONES DE ALTURA

AUTOR:
José María Tintero Navajas

REVISOR:
Maya Ruiz Díaz

ESCALA:
1:200

COTAS EN:
m

AUTOR:

TITULACIÓN:
GRADO EN INGENIERÍA ELECTRÓNICA, ROBÓTICA Y MECATRÓNICA

FECHA:
JUNIO/2026

REVISOR:

Fdo.: