

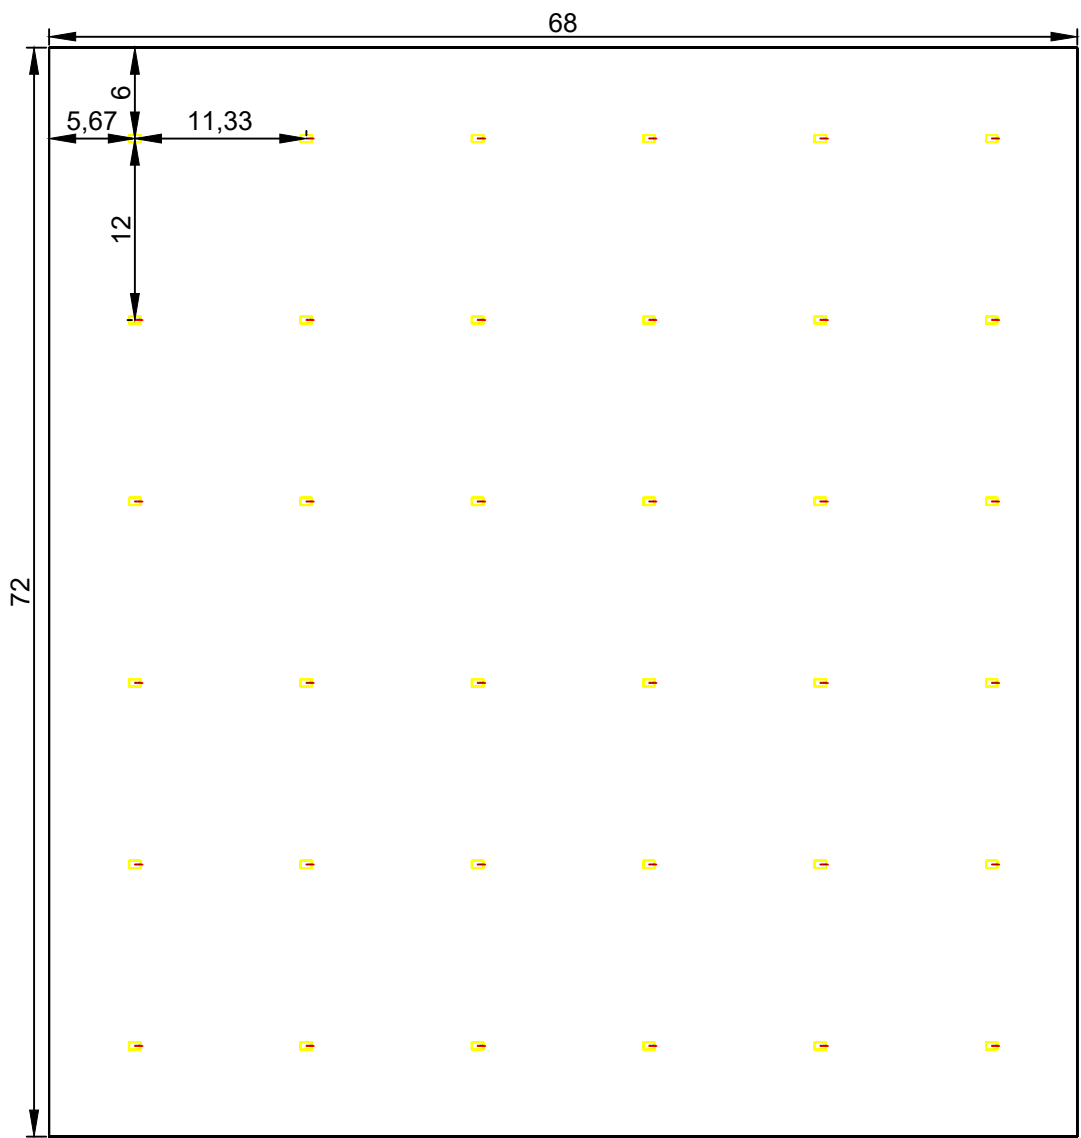


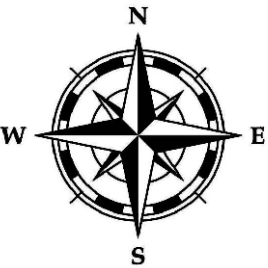

NOTAS

- 1. Altura de montaje de luminarias: 25,7 m sobre el suelo
- 2. Em diseño = 1052 lx al 100% de flujo
- 3. Densidad de potencia instalada: 8,8 W/m²
- 4. Todas las luminarias incorporan driver DALI para regulación conforme a Tablas 1 y 2 del proyecto
- 5. La distribución es matricial uniforme 6 × 6 ud
- 6. Superficie del taller: 4896 m²

LEYENDA					
Símbolo	Referencia	Descripción	Potencia (W)	Flujo (lm)	Cantidad
	PRYLUX 678155 ASTRANI 6X96L 1200W 740 100-277V 30° IP66 9007 DALI-678155	Luminaria LED industrial suspendida	1200	178149	36 Piezas

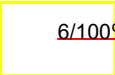

UNIVERSIDAD DE MÁLAGA

PROYECTO DE INGENIERÍA:
Iluminación automatizada y sistema de videovigilancia del hangar 3 de
producción de aviones. Fábrica AIRBUS - Tablada (Sevilla)

PROMOTOR: Airbus S.A.S.		LOCALIZACIÓN: Av. Maestranza Aérea, Nº 17, C.P. 41011, Sevilla (España)				
PLANO Nº: 2.1.	DISTRIBUCIÓN DE LUMINARIAS EN LA SECCIÓN CENTRAL					
AUTOR: José María Tendero Navajas		REVISOR: Maya Ruiz Díaz		ESCALA: 1:500	COTAS EN: m	AUTOR:
TITULACIÓN: GRADO EN INGENIERÍA ELECTRÓNICA, ROBÓTICA Y MECATRÓNICA		FECHA: JUNIO/2026			REVISOR:	
					Fdo.:	