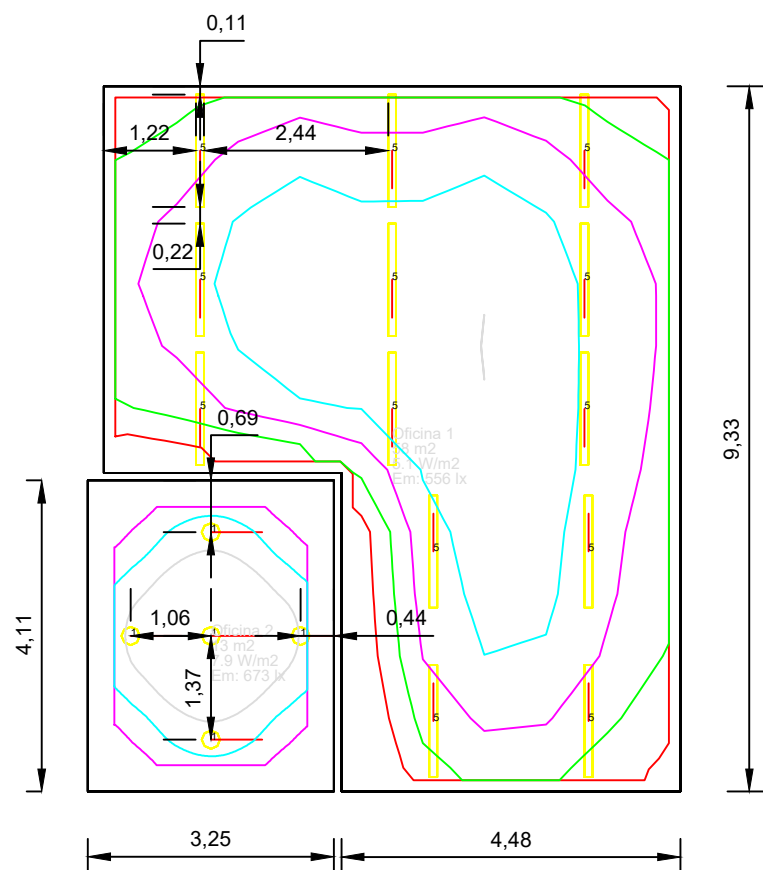
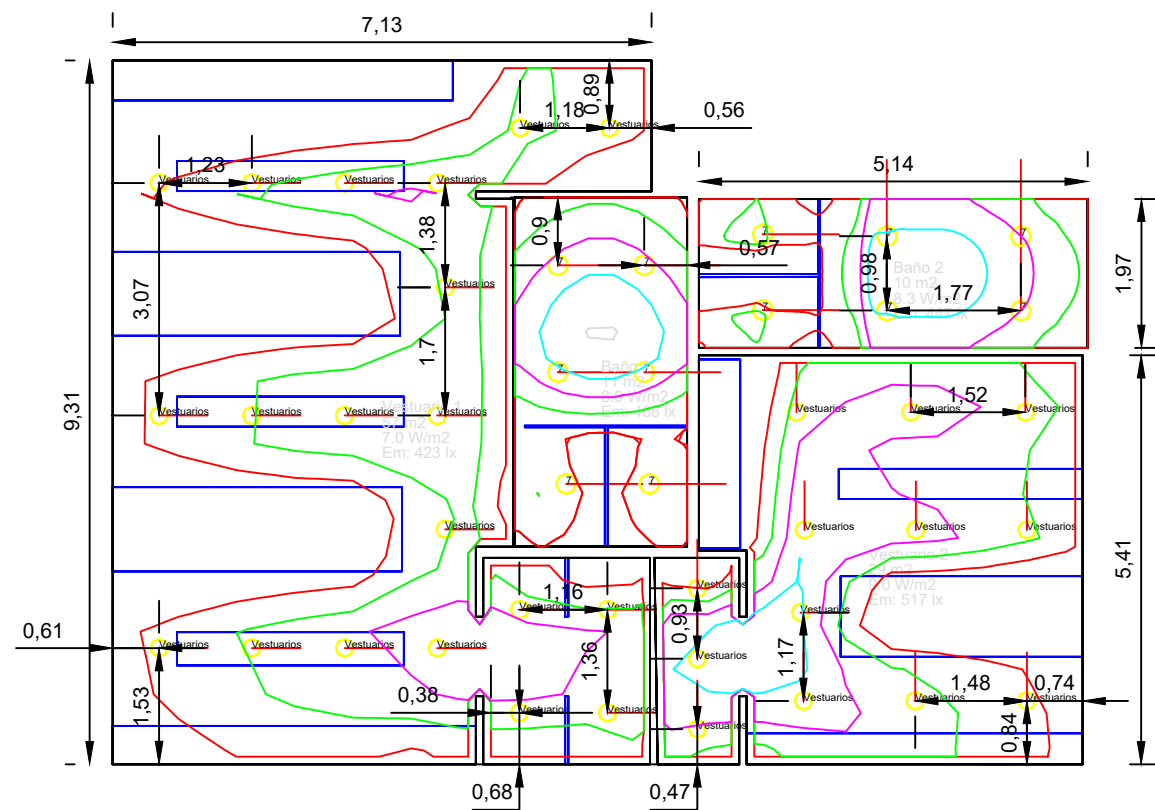


LEYENDA						
Símbolo	Referencia	Descripción	Potencia (W)	Flujo (lm)	IP	Cantidad
	brand Signify, Philips 910505103609 DN142B 20S/840 PSD-E WR D200 ELB3	Downlight LED empotrado estanco	37,5	5900	IP44	33
	ZUMTOBEL 62927749 (STD - Standard) PANOS R R150 2k-940 LDO H AL RET WH	Downlight LED empotrado redondo	14,1	1940	IP44	12
	brand Signify, Philips 911401842487 SM136V G4 36_45_68S/840 PSD W20L157 OC	Luminaria LED lineal empotrada	22,5	6800	IP20	13
	brand Signify, Philips 910505102289 DN470B LED30S/840 PSD-E C WH P	Downlight LED empotrado	21,2	2900	IP20	5

ISOLÍNEAS	
	300,0 lx
	400,0 lx
	500,0 lx
	600,0 lx
	700,0 lx

NOTAS
- Luminarias empotradas en falso techo existente - Control automatizado conforme al CTE DB-HE3 - Niveles mínimos según UNE-EN 12464-1: - Oficinas: $Em \geq 500 \text{ lx}$ / $UGR \leq 19$ / $Ra \geq 80$ - Vestuarios y baños: $Em \geq 200 \text{ lx}$ / $UGR \leq 25$ / $Ra \geq 80$ - Resultados obtenidos en DIALux: - Oficina 1: $Em = 556 \text{ lx}$ - Oficina 2: $Em = 673 \text{ lx}$ - Vestuario 1: $Em = 423 \text{ lx}$ - Vestuario 2: $Em = 517 \text{ lx}$ - Baño 1: $Em = 468 \text{ lx}$ - Baño 2: $Em = 447 \text{ lx}$ - Luminarias con driver DALI para regulación - IP mínimo en baños y vestuarios: IP44

 AIRBUS		UNIVERSIDAD DE MÁLAGA			
		PROYECTO DE INGENIERÍA: Iluminación automatizada y sistema de videovigilancia del hangar 3 de producción de aviones. Fábrica AIRBUS - Tablada (Sevilla)			
PROMOTOR: Airbus S.A.S.		LOCALIZACIÓN: Av. Maestranza Aérea, Nº 17, C.P. 41011, Sevilla (España)			
PLANO Nº: 2.3.	DISTRIBUCIÓN DE LUMINARIAS EN OFICINAS, VESTUARIOS Y BAÑOS				
AUTOR: José María Tendaro Navajas	REVISOR: Maya Ruiz Díaz	ESCALA: 1:100	COTAS EN: m	AUTOR:	
TITULACIÓN: GRADO EN INGENIERÍA ELECTRÓNICA, ROBÓTICA Y MECATRÓNICA		FECHA: JUNIO/2026		REVISOR:	
				Fdo.:	