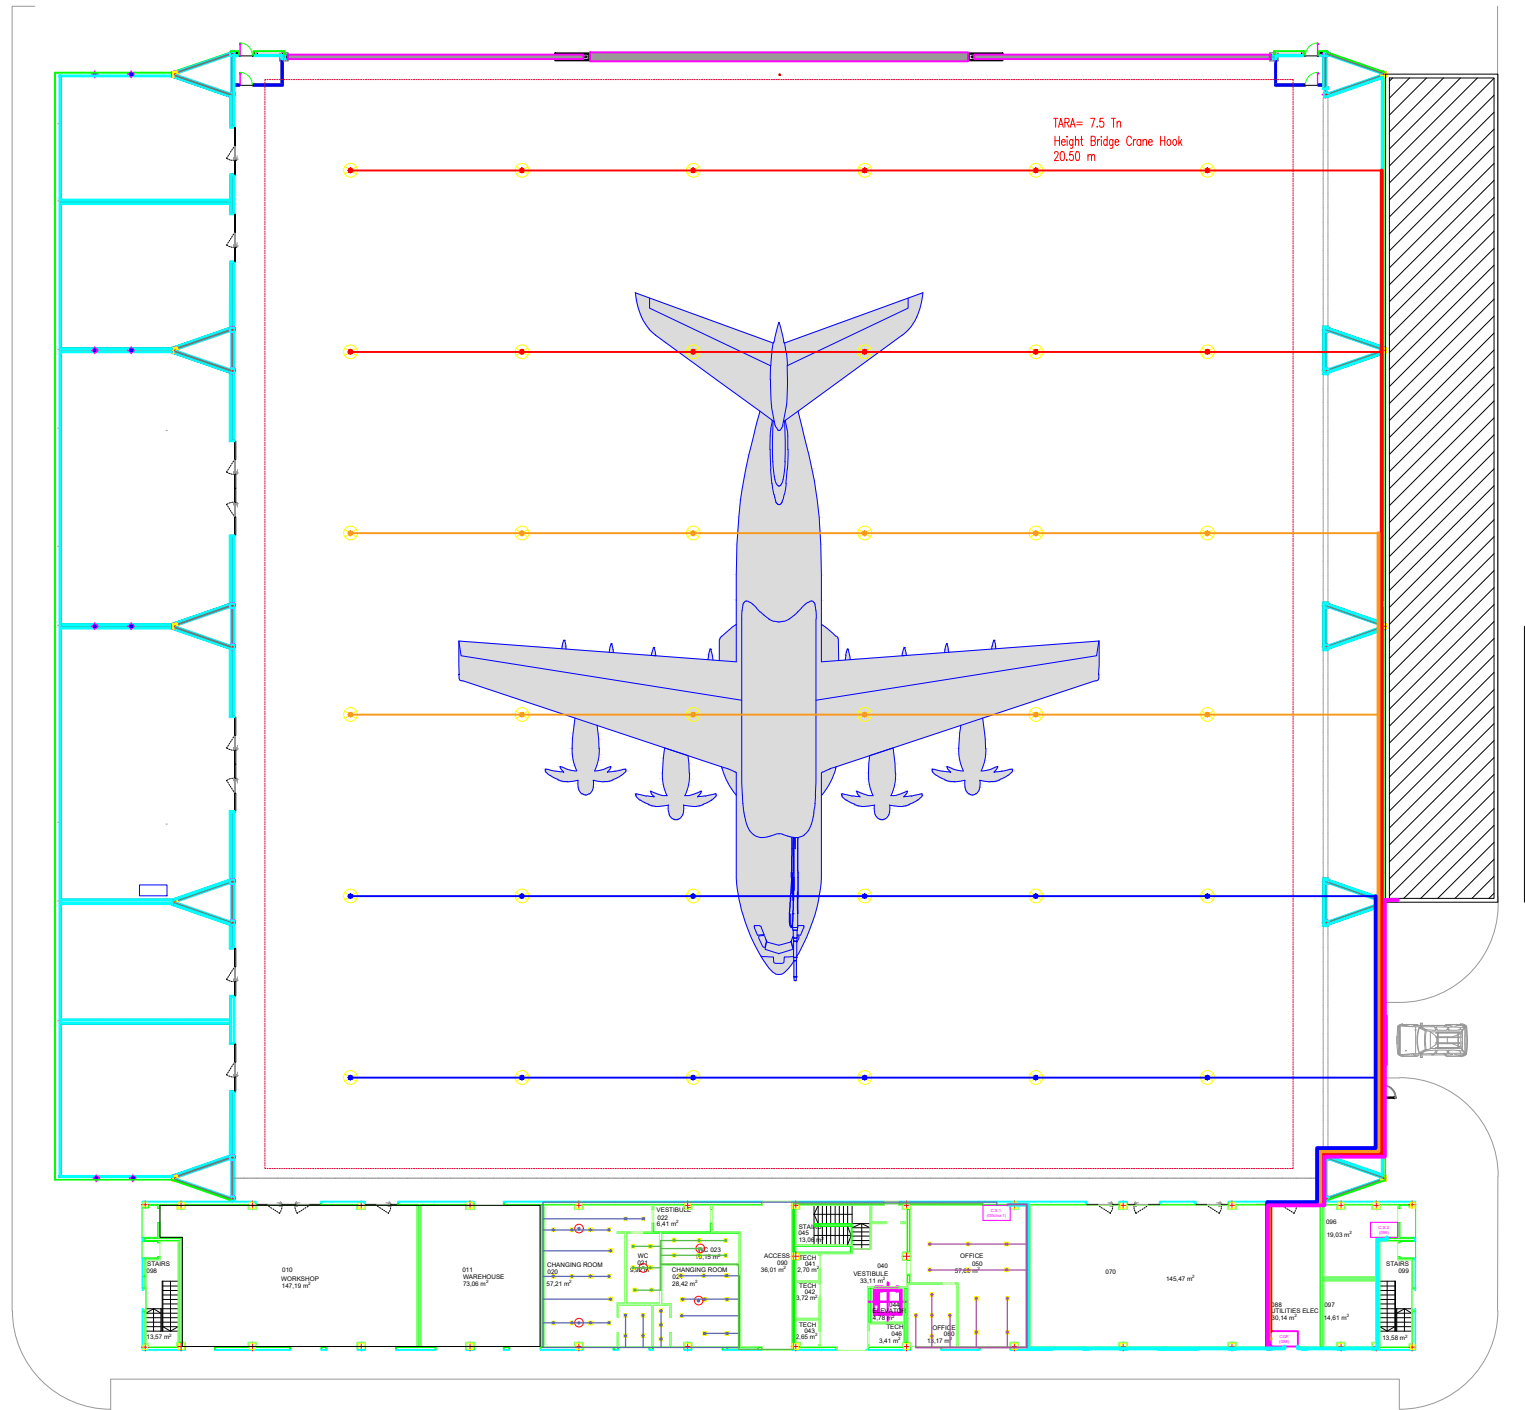


LEYENDA	
Línea	Referencia
	Línea circuito L-H1 — Hangar central, circuito 1 (luminarias grupo 1)
	Línea circuito L-H2 — Hangar central, circuito 2 (luminarias grupo 2)
	Línea circuito L-H3 — Hangar central, circuito 3 (luminarias grupo 3)
	Líneas de consumo L-A — Almacén longitudinal
	Alimentación eléctrica cuadros secundarios (C.S.1 oficina / C.S.2 sala 096)
	Líneas de consumo CS1-L1 — Oficinas
	Líneas de consumo CS1-L2 — Vestuarios
	Líneas de consumo CS1-L3 — Baños

NOTAS

1. Plano de distribución en planta a cota ±0,00. Las líneas de consumo se representan de forma esquemática; el trazado exacto se definirá en obra conforme al Pliego de Condiciones.

2. No se desarrolla en este plano la acometida, la LGA ni la derivación individual, conforme a las especificaciones particulares del cliente.

3. El Cuadro Principal de Protecciones (C.P.) y la centralita de control DALI se ubican en la estancia 088. Los cuadros secundarios C.S.1 (oficinas) y C.S.2 (sala 096) se muestran en su posición en planta.

4. Las líneas de consumo de la sección central del hangar se agrupan en 3 circuitos independientes (L-H1, L-H2, L-H3), conforme al esquema unifilar Plano 5.2.3.

5. Las canalizaciones eléctricas se realizarán mediante bandeja de rejilla de acero galvanizado en zonas industriales (hangar y almacén) y tubo rígido de PVC M32 IP55 en oficinas, vestuarios y aseos, según especificaciones del Pliego de Condiciones.

6. Las líneas del bus DALI-2 y las líneas de alimentación de luminarias discurren por la misma bandeja, debidamente segregadas conforme al REBT ITC-BT-21.

7. Las secciones de los conductores y los elementos de protección (PIA, diferenciales) están justificados en el Anexo X — Cálculos justificativos de la instalación eléctrica de baja tensión.

8. El cableado del sistema de videovigilancia (Cat 6A AWG23 PoE+ y fibra óptica OM3/OS2) discurre por canalizaciones independientes de las líneas eléctricas de alimentación, conforme a lo indicado en los Planos 4.1 y 4.2.

9. Para los esquemas unifilares de los cuadros eléctricos, ver Planos 5.2.1, 5.2.2 y 5.2.3.

UNIVERSIDAD DE MÁLAGA

PROYECTO DE INGENIERÍA:

Iluminación automatizada y sistema de videovigilancia del hangar 3 de producción de aviones. Fábrica AIRBUS - Tablada (Sevilla)

PROMOTOR:
Airbus S.A.S.

LOCALIZACIÓN:
Av. Maestranza Aérea, Nº 17, C.P. 41011, Sevilla (España)

PLANO Nº:
5.1.1.

LÍNEAS DE CONSUMO DEL HANGAR Y OFICINAS

AUTOR:
José María Tendaro Navajas

REVISOR:
Alejandro Sánchez Monterroso

ESCALA:
1:500

COTAS EN:
-

AUTOR:

TITULACIÓN:
GRADO EN INGENIERÍA ELECTRÓNICA, ROBÓTICA Y MECATRÓNICA

FECHA:
JUNIO/2026

REVISOR:

Fdo.: