


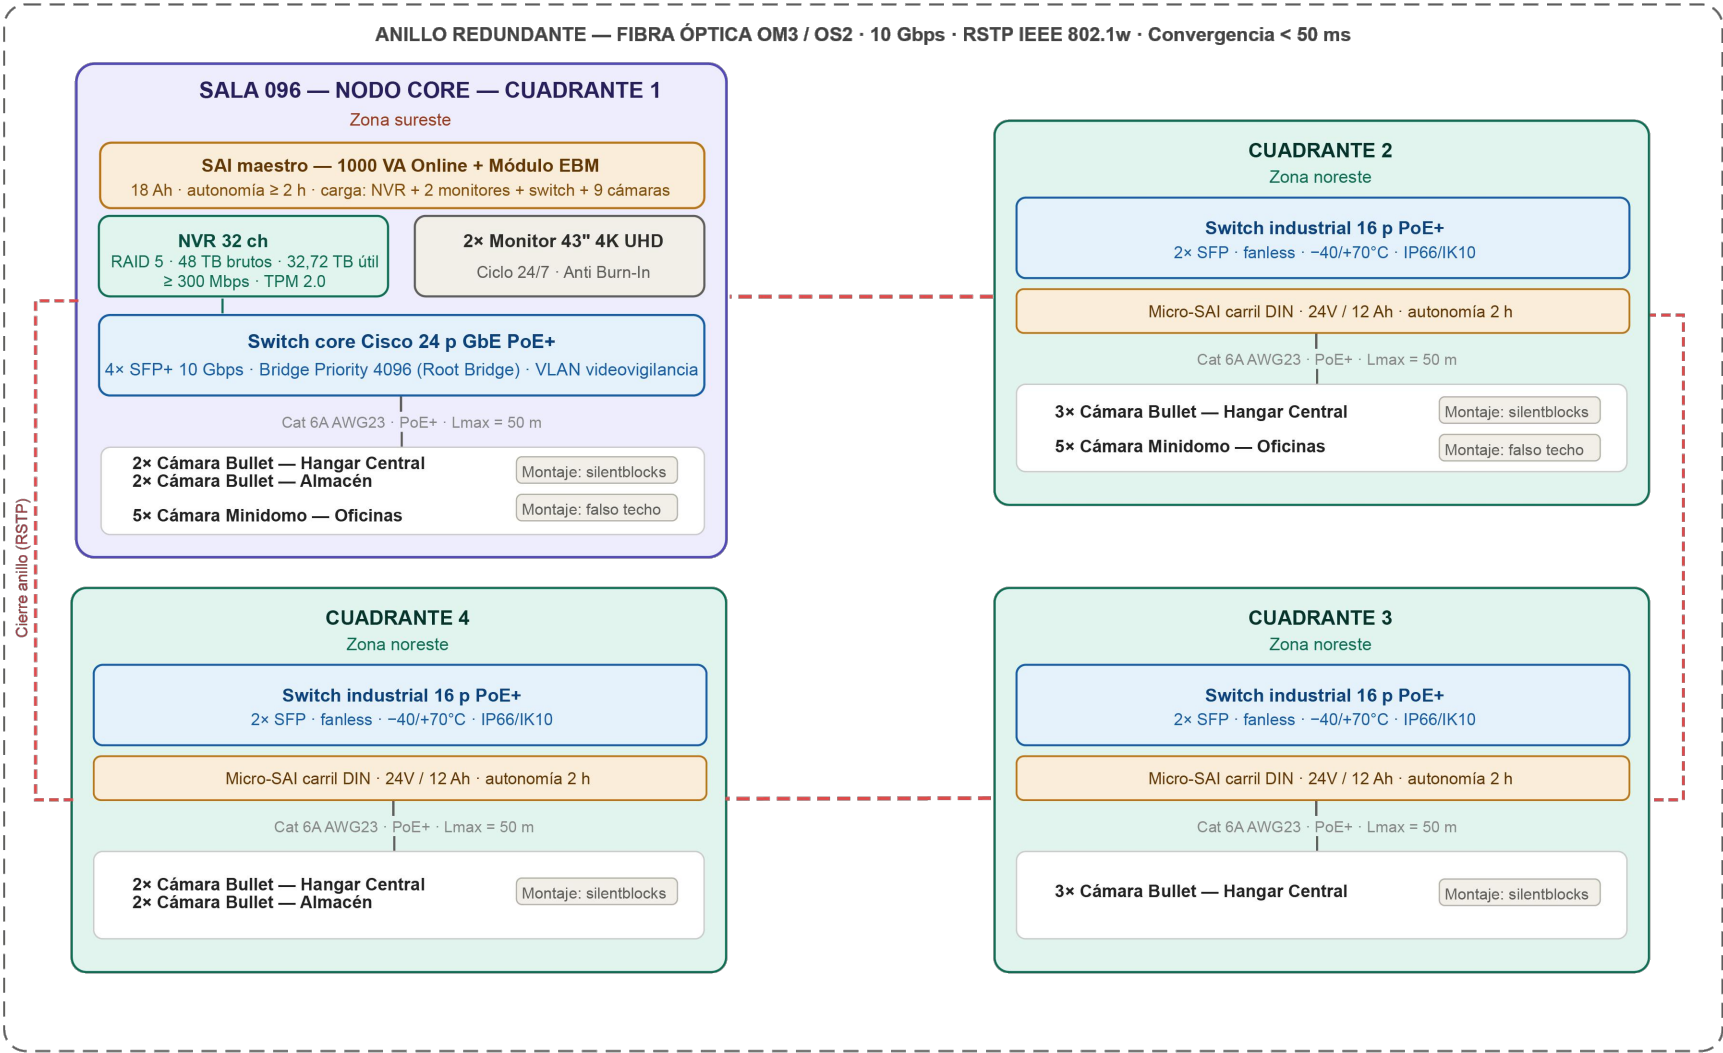

LEYENDA	
Switch core (sala 096) Cisco 24p SFP+ Root Bridge RSTP · Bridge Priority 4096 370 W PoE budget · ocup. 24,3%	Anillo fibra óptica OM3/OS2 · SFP+ 10 Gbps · RSTP Convergencia < 50 ms ante corte Pérdida máx. 0,5 dB/evento (OTDR)
Switch industrial campo (x4) 16p PoE+ · 2× SFP Fanless · IP66/IK10 · -40/+70°C Port Security Sticky MAC · VLAN CCTV	SAI maestro + micro-SAIs campo 1000 VA + EBM 4× micro-SAI DIN 24V/12 Ah campo Autonomía ≥ 2 h todo el sistema Vol. ahorro micro-SAI DIN: 86,9%

Tráfico total: 72 Mbps (0,86% del troncal 10 Gbps) · Protocolo: H.265+ VBR · VLAN dedicada · Port Security Sticky MAC · NTP común
Retención imágenes: 30 días máx. conforme LO 3/2018 (LOPDGDD) Art. 22.3 · Certificación pasiva: Fluke TIA/EIA-568 Cat 6A + OTDR fibra

 AIRBUS		UNIVERSIDAD DE MÁLAGA			
PROYECTO DE INGENIERÍA: Iluminación automatizada y sistema de videovigilancia del hangar 3 de producción de aviones. Fábrica AIRBUS - Tablada (Sevilla)					
PROMOTOR: Airbus S.A.S.			LOCALIZACIÓN: Av. Maestranza Aérea, Nº 17, C.P. 41011, Sevilla (España)		
PLANO Nº: 5.2.2.	ESQUEMA DE VIDEOVIGILANCIA Y SEGURIDAD				
AUTOR: José María Tendaro Navajas		REVISOR: David Sánchez Jiménez		ESCALA: -	COTAS EN: -
TITULACIÓN: GRADO EN INGENIERÍA ELECTRÓNICA, ROBÓTICA Y MECATRÓNICA			FECHA: JUNIO/2026		AUTOR: REVISOR: Fdo.: