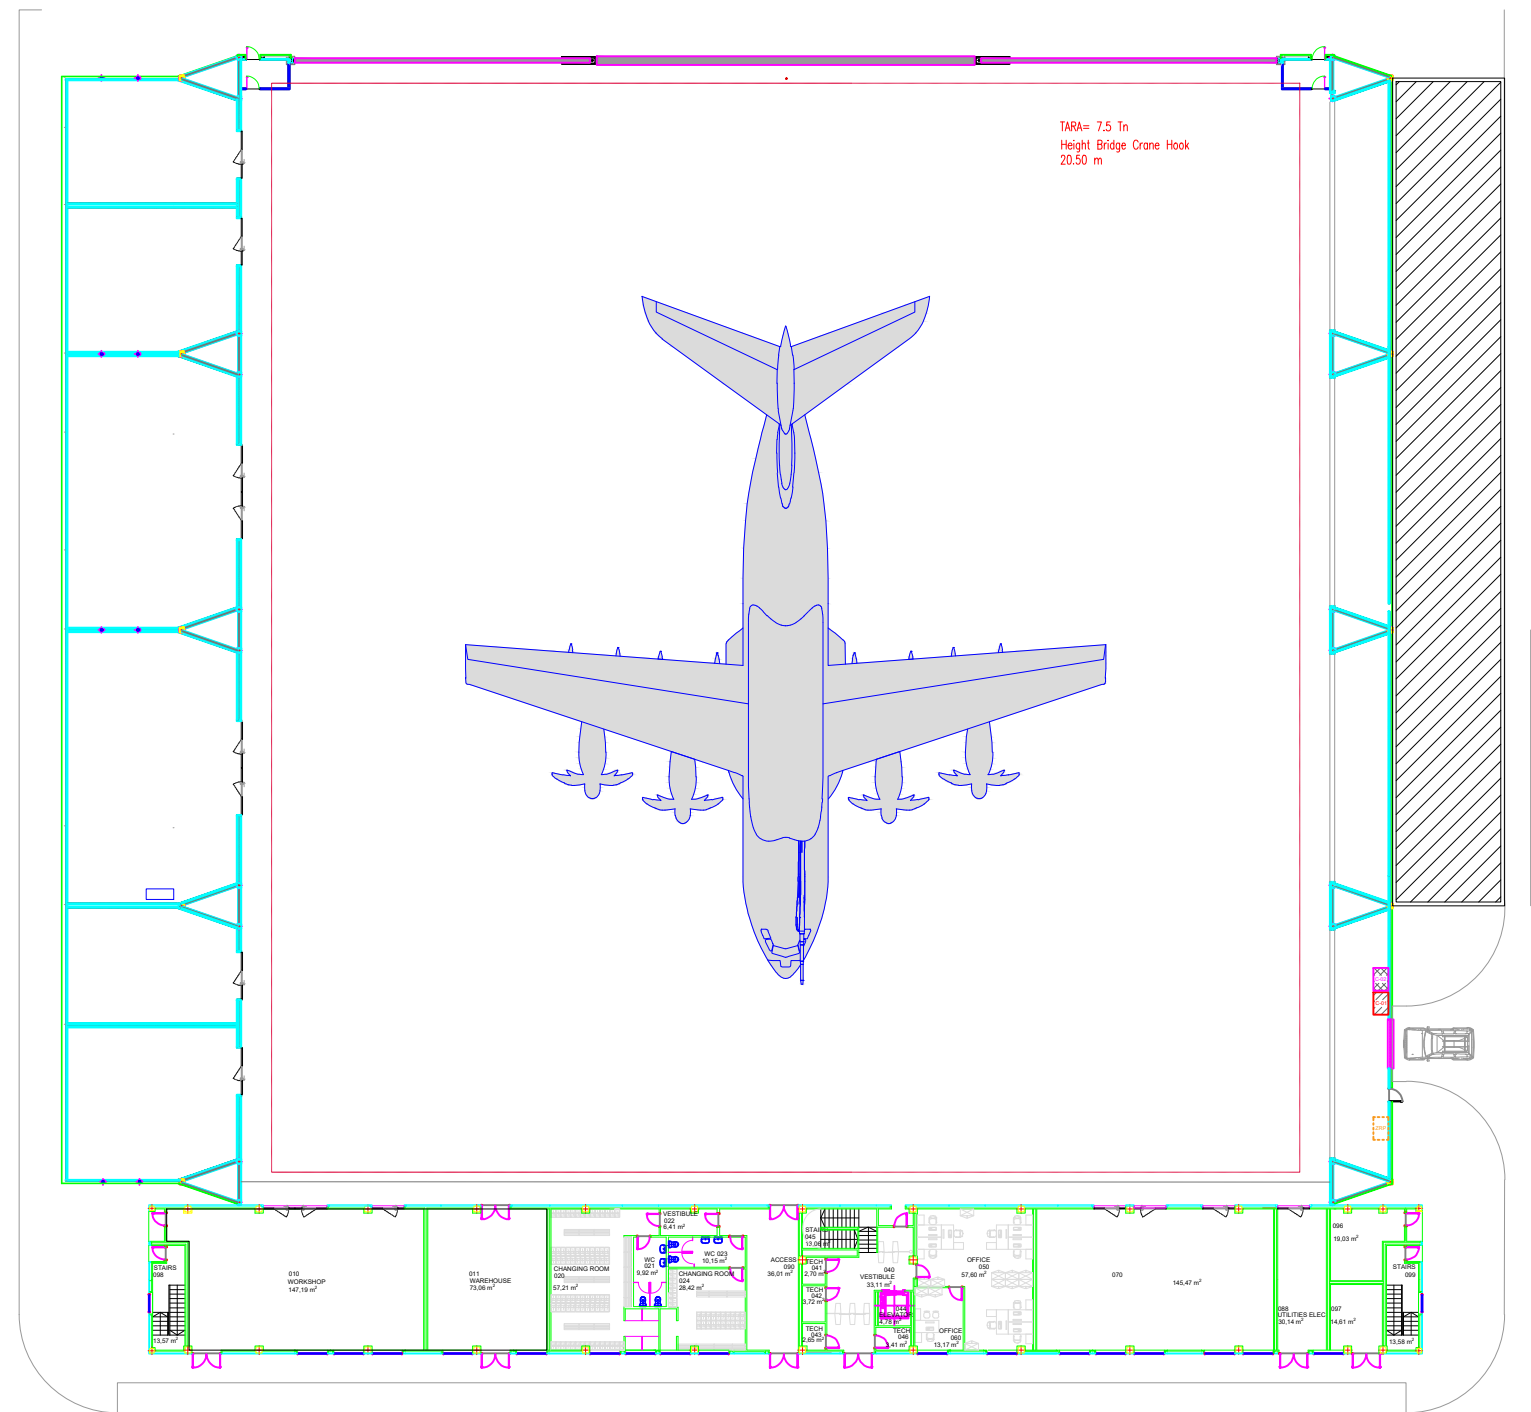


LEYENDA		
Símbolo	Referencia	Descripción
	C-01	Contenedor — Residuos inertes no valorizables (cartón, espumas, plásticos). Retirada a vertedero autorizado.
	C-02	Contenedor — Residuos valorizables (metales, cable eléctrico, PVC estructural). Entrega a gestor valorizable autorizado con documentación de seguimiento.
	ZRP	Zona habilitada — Residuos peligrosos y RAEE (baterías, pilas, equipos electrónicos retirados). Almacenamiento temporal en recipientes homologados hasta retirada por ARD autorizado con DCS.

NOTAS
1. Plano de gestión de RCD a cota ±0,00. Las ubicaciones de los puntos de acopio son provisionales durante la fase de ejecución; podrán ajustarse en obra previo acuerdo con el Coordinador de Seguridad y Salud.
2. En obra se dispondrán al menos dos contenedores diferenciados y señalizados conforme al RD 105/2008: C-01 para inertes no valorizables y C-02 para valorizables.
3. Los residuos peligrosos (baterías SAI, pilas) y los RAEE (cámaras, drivers y equipos de control retirados) se almacenarán en la zona ZRP, en recipientes homologados y debidamente etiquetados, hasta su retirada por gestor ARD autorizado con emisión del correspondiente Documento de Control y Seguimiento (DCS). Ver Anexo XI, A.XI.4.
4. Los equipos electrónicos desechados (RAEE) se entregarán a punto de recogida de un Sistema Integrado de Gestión RAEE autorizado, conforme al RD 110/2015.
5. Queda prohibido el depósito de residuos fuera de los puntos de acopio señalizados. Cada contenedor dispondrá de señalización normalizada con la fracción admitida.
6. El contratista llevará registro documental de cantidad, tipología y destino de cada fracción, a disposición de la Dirección de Obra en todo momento.

 AIRBUS	UNIVERSIDAD DE MÁLAGA			
	PROYECTO DE INGENIERÍA: Iluminación automatizada y sistema de videovigilancia del hangar 3 de producción de aviones. Fábrica AIRBUS - Tablada (Sevilla)			
PROMOTOR: Airbus S.A.S.		LOCALIZACIÓN: Av. Maestranza Aérea, Nº 17, C.P. 41011, Sevilla (España)		
PLANO Nº: 6.1.	UBICACIÓN DE CONTENEDORES PARA LA GESTIÓN DE RESIDUOS			
AUTOR: José María Tendaro Navajas	REVISOR: Maya Ruiz Díaz	ESCALA: 1:500	COTAS EN: -	AUTOR:
TITULACIÓN: GRADO EN INGENIERÍA ELECTRÓNICA, ROBÓTICA Y MECATRÓNICA		FECHA: JUNIO/2026		REVISOR:
				Fdo.: